


----- 108年度
 ----- 109年度
 ----- 110年度
 ----- 112年01月
 ----- 113年01月
 ----- 113年12月

----- 106年度
 ----- 107年度

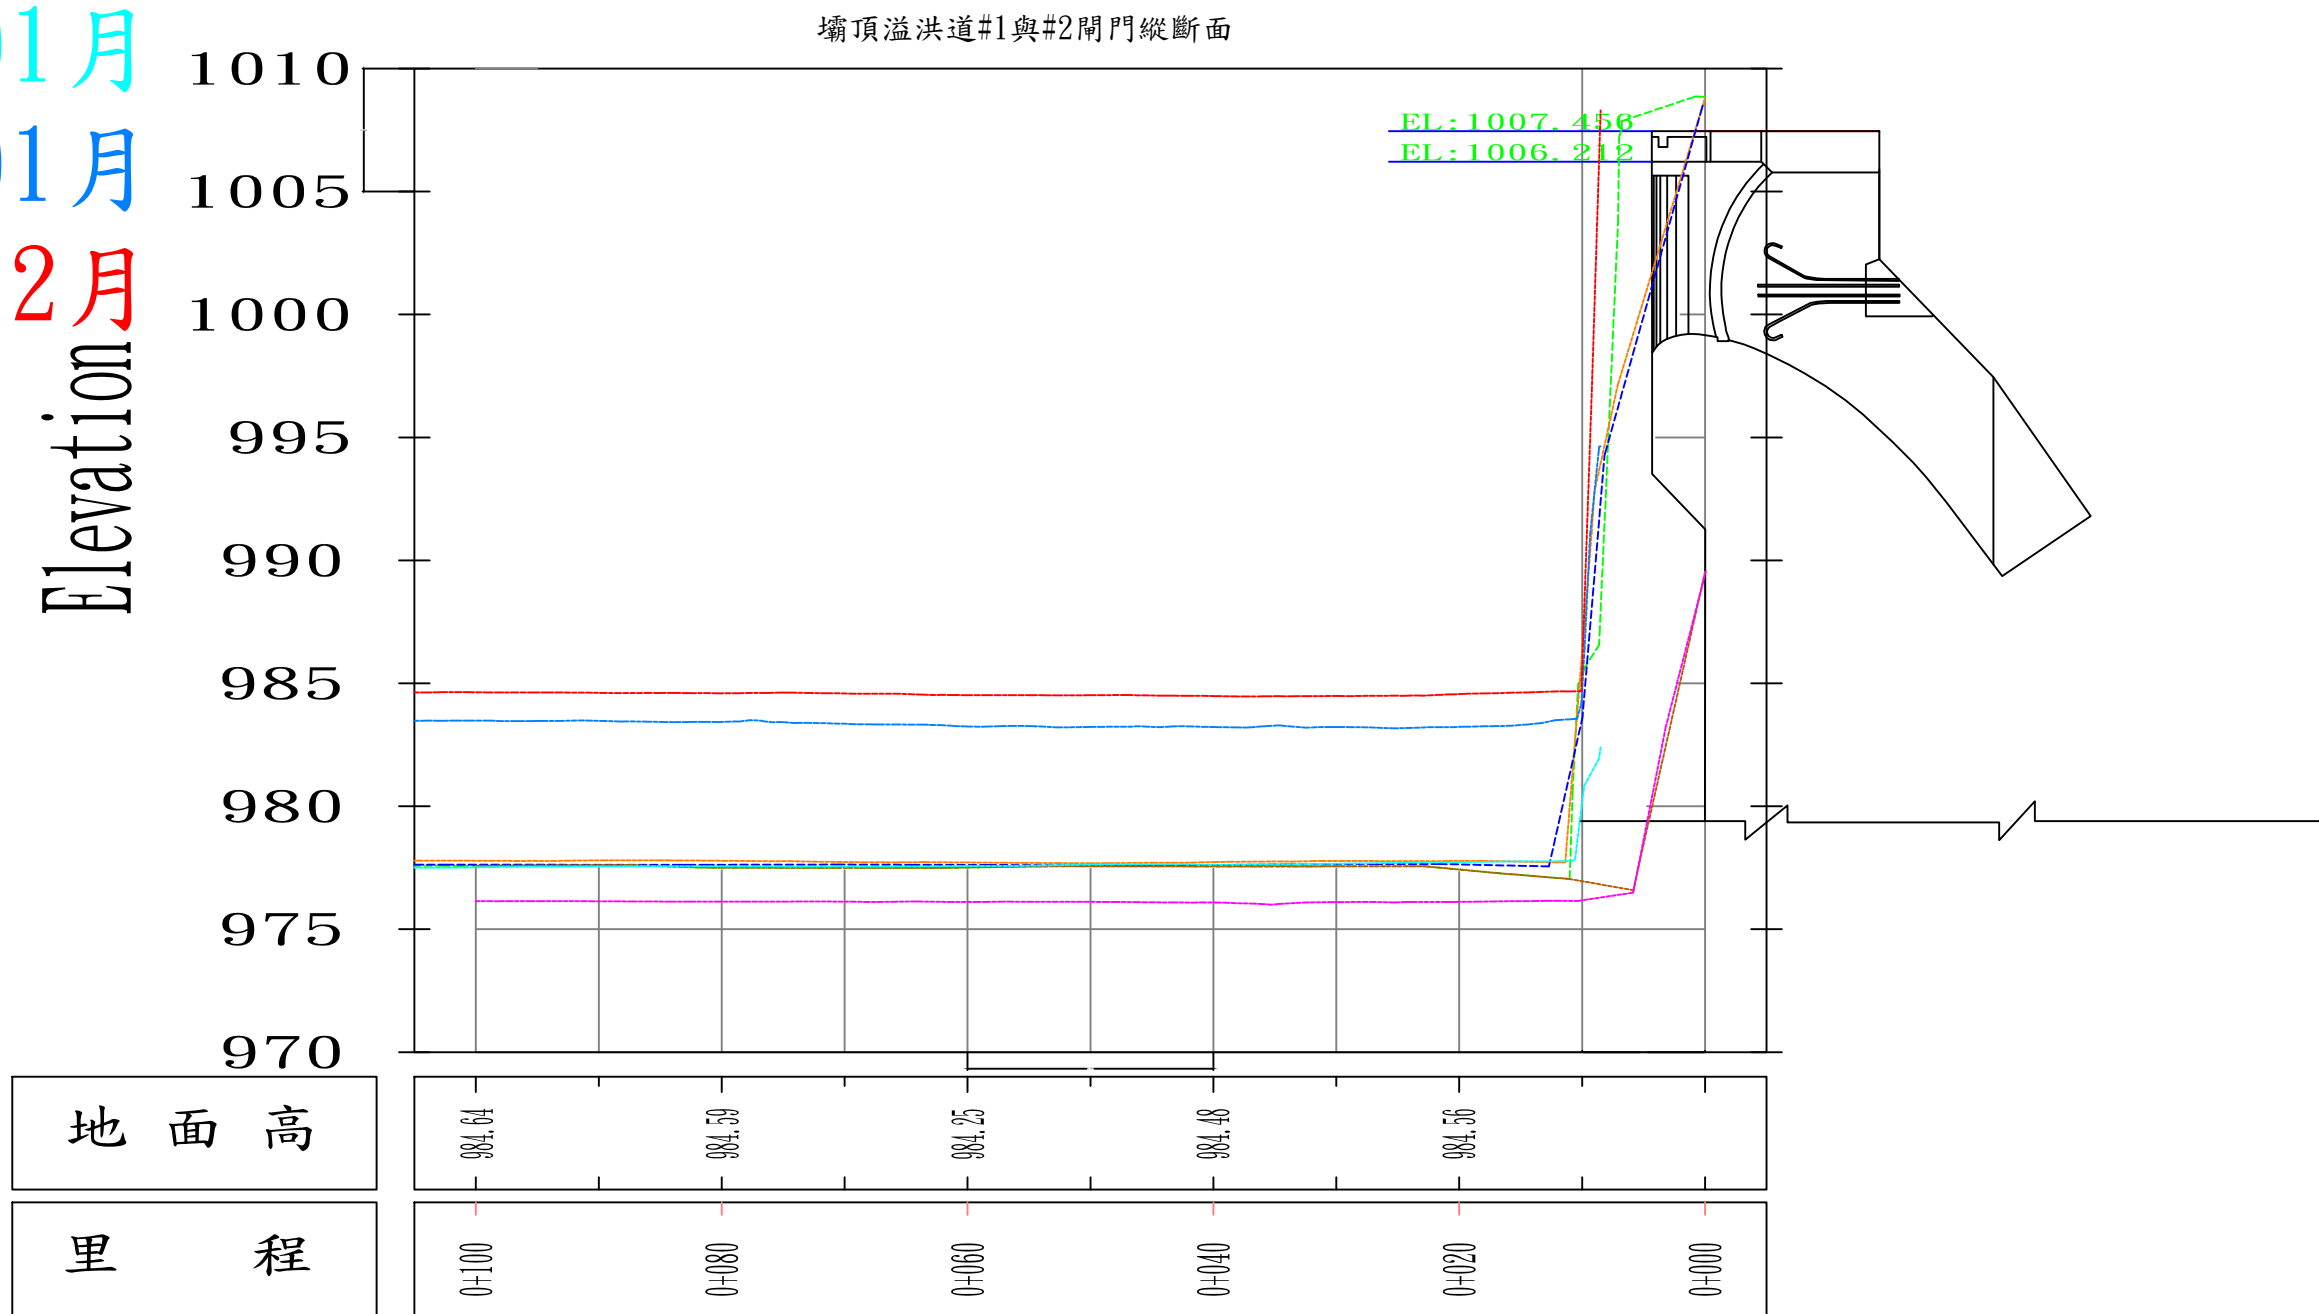

D' <---D

(4)壩頂溢洪道#1與#2閘門前100公尺縱斷面圖

圖面比例S= $\frac{Y=1/312.5}{X=1/615}$