


----- 110年度	----- 106年度
----- 112年01月	----- 107年度
----- 113年01月	----- 108年度
----- 113年12月	----- 109年度

第#1與#2機組發電進水口閘門(攔汙柵)縱斷面

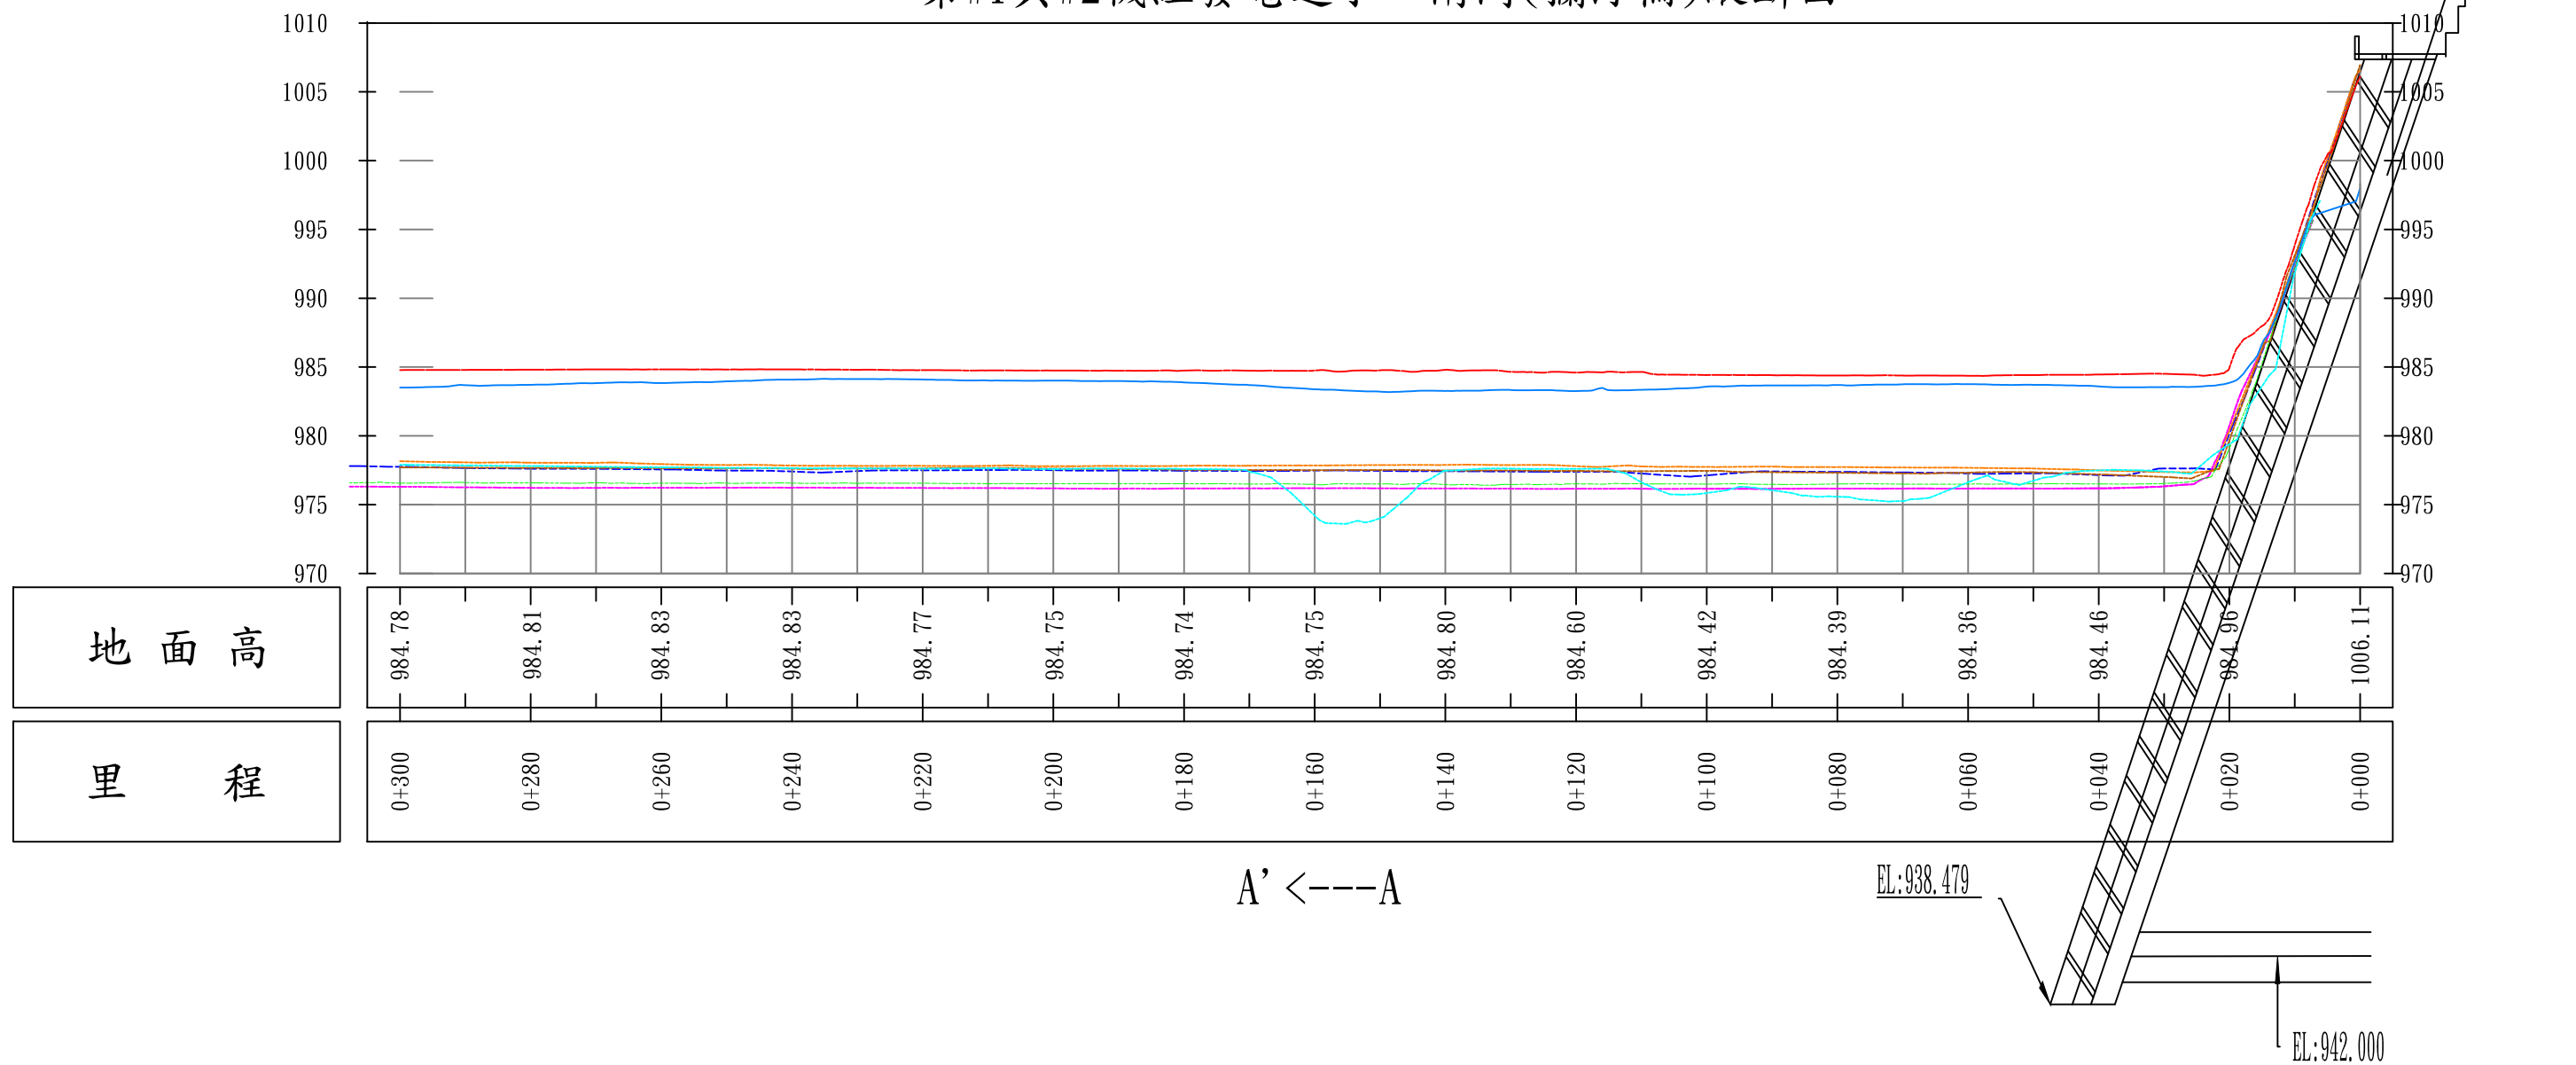


(1)第#1與#2機組發電進水口閘門(攔汙柵)前300公尺縱斷面圖

圖面比例S= $\frac{Y=1/500}{X=1/1026}$

----- 110年度	----- 106年度
----- 112年01月	----- 107年度
----- 113年01月	----- 108年度
----- 113年12月	----- 109年度

第#4機組發電進水口閘門(攔汙柵)縱斷面

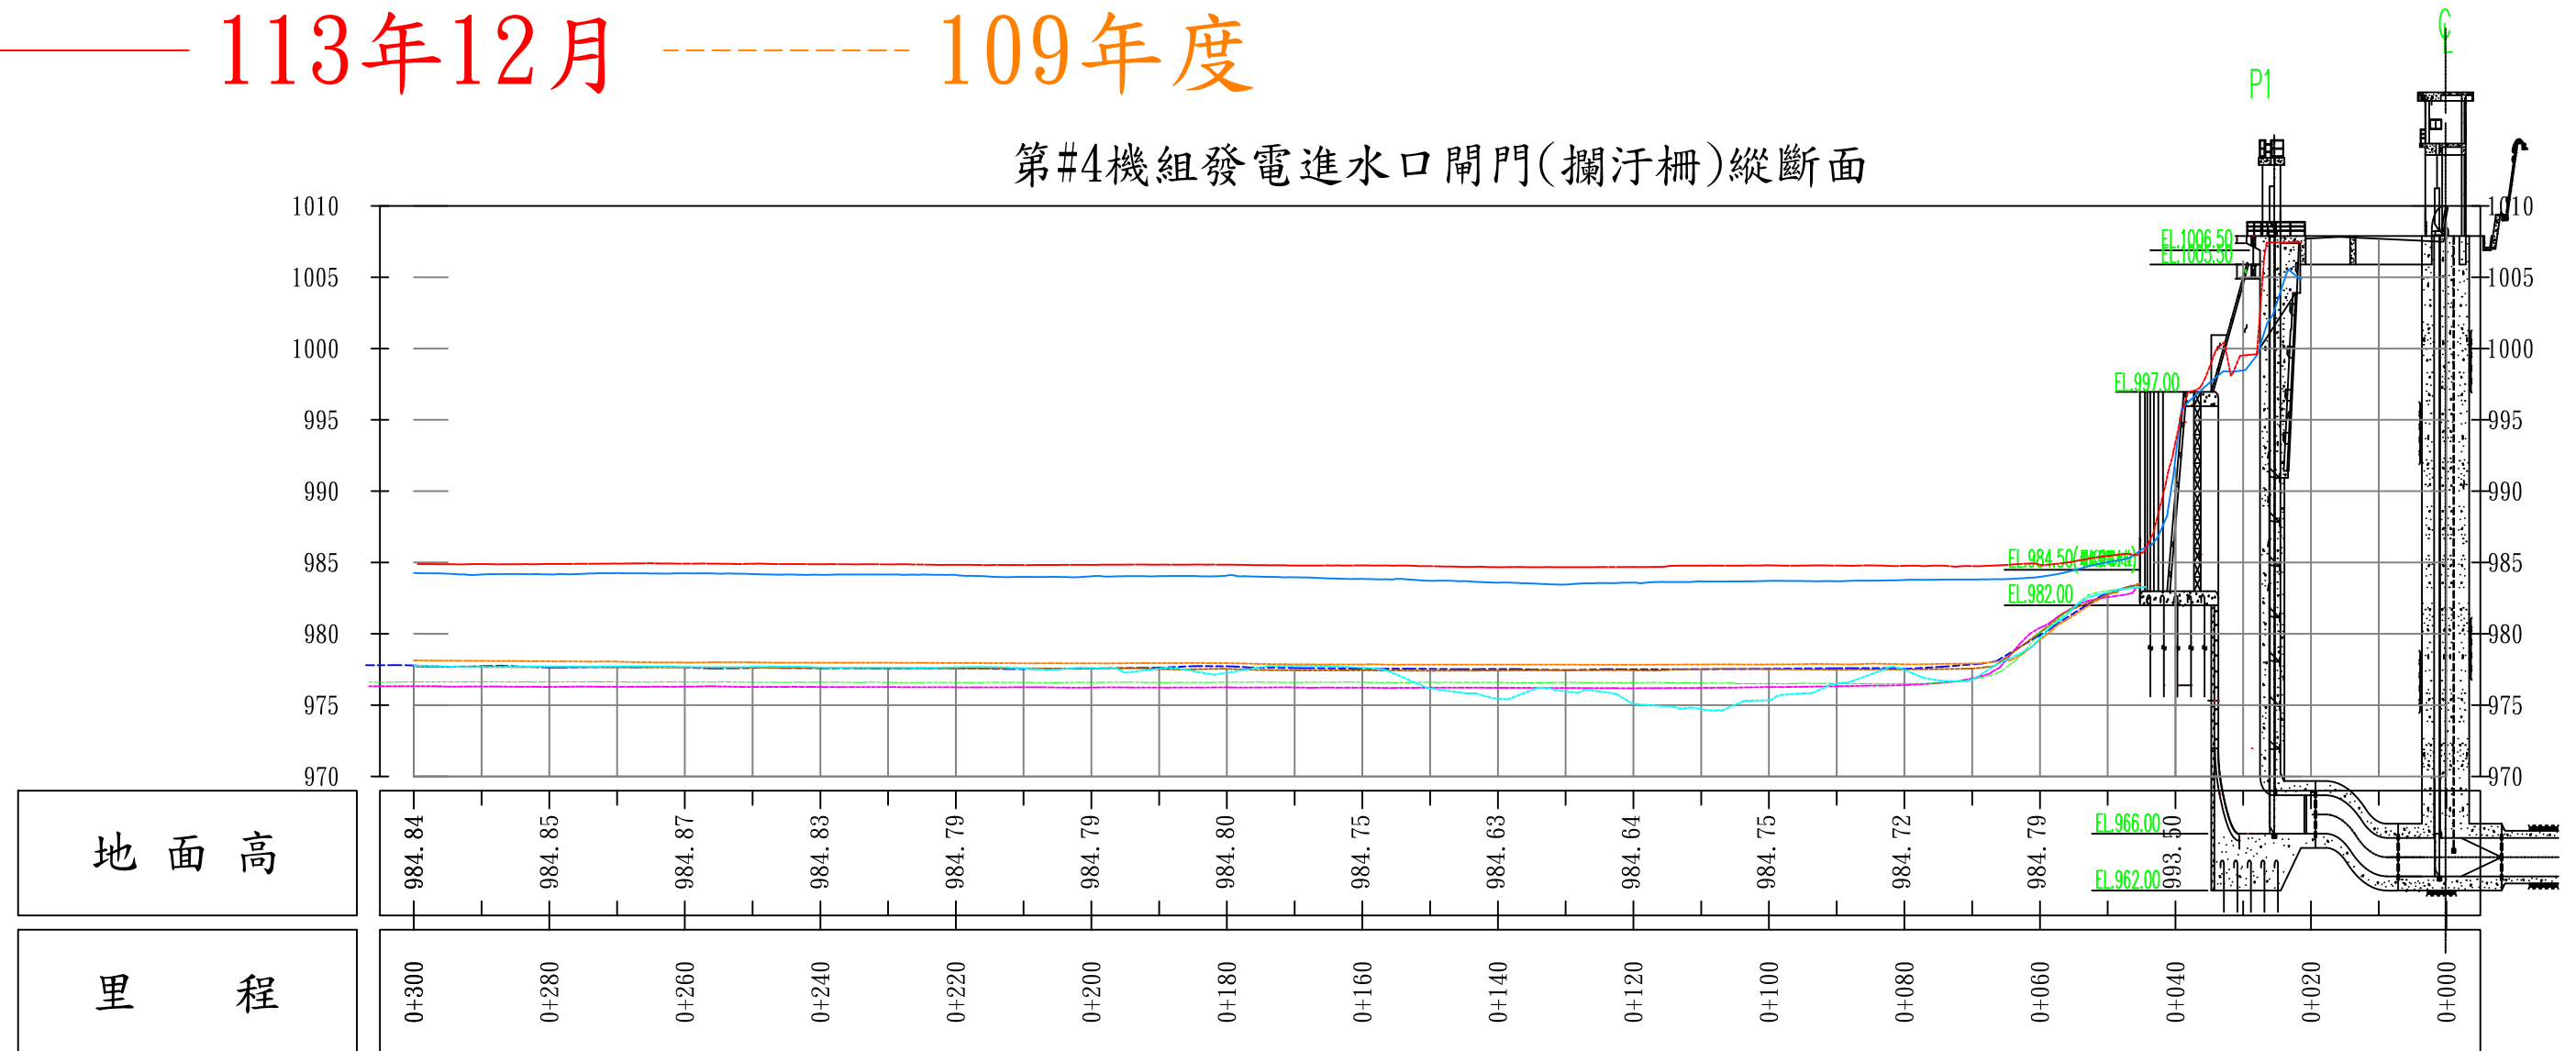


B' <---B

(2)第#4機組發電進水口閘門(攔汙柵)前300公尺縱斷面圖


圖面比例S= $\frac{Y=1/500}{X=1/1026}$


- | | |
|---------------|-------------|
| ----- 110年度 | ----- 106年度 |
| ----- 112年01月 | ----- 107年度 |
| ----- 113年01月 | ----- 108年度 |
| ----- 113年12月 | ----- 109年度 |

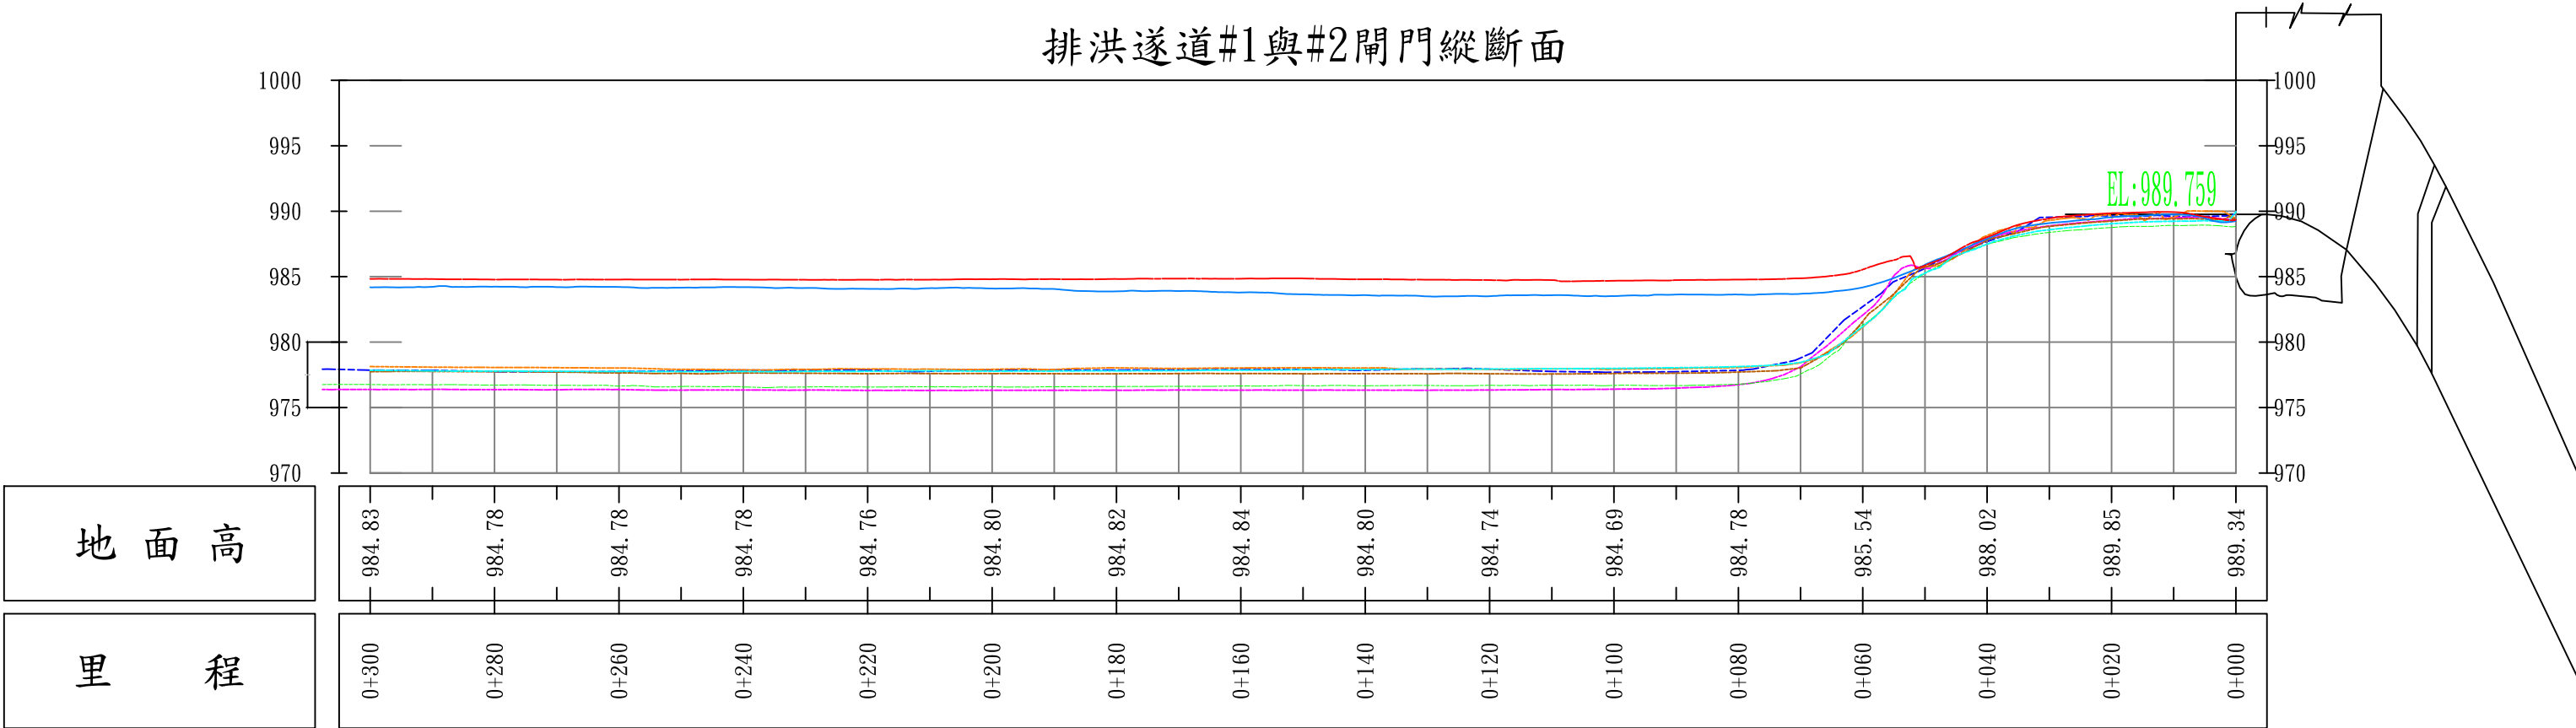


C' <---C

(3)排洪隧道#1與#2閘門前300公尺縱斷面圖

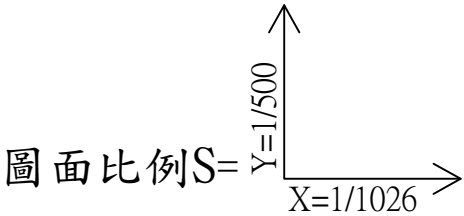


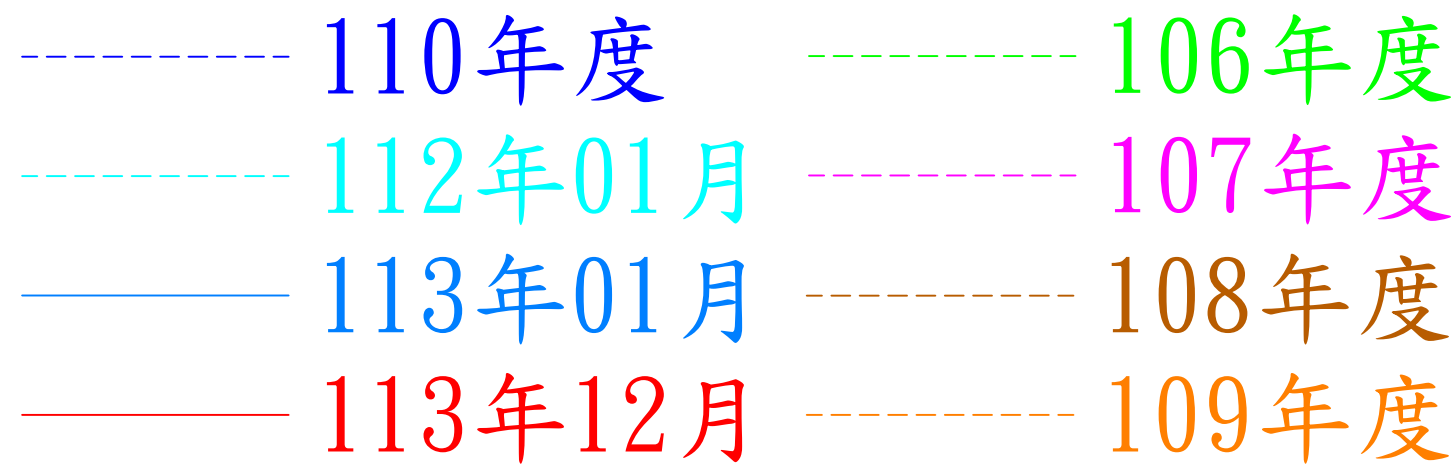

壩頂溢洪道#1與#2閘門縱斷面

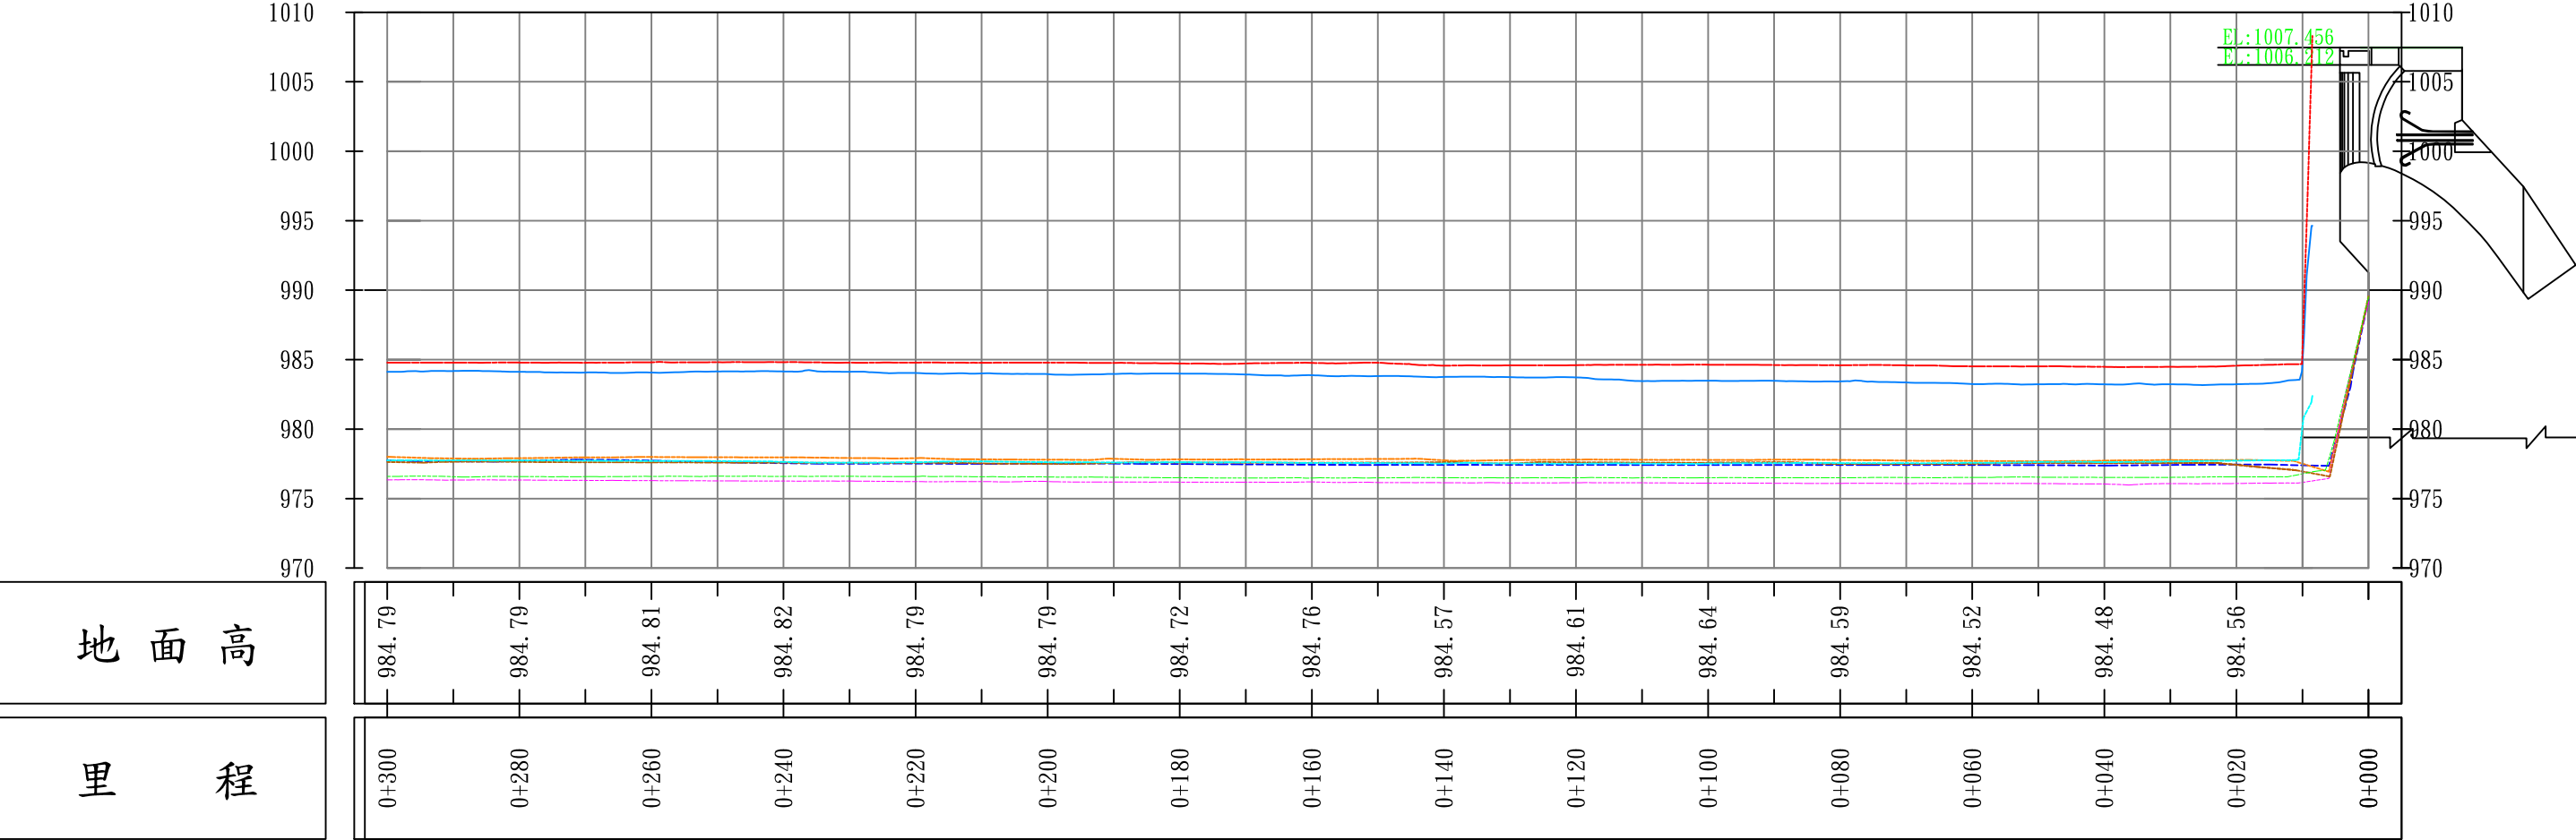

D' <---D

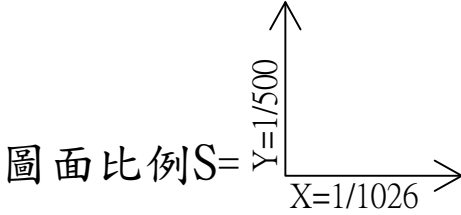

(4)壩頂溢洪道#1與#2閘門前300公尺縱斷面圖