


- |               |             |
|---------------|-------------|
| ----- 110年度   | ----- 106年度 |
| ----- 112年01月 | ----- 107年度 |
| ----- 113年01月 | ----- 108年度 |
| ----- 113年12月 | ----- 109年度 |

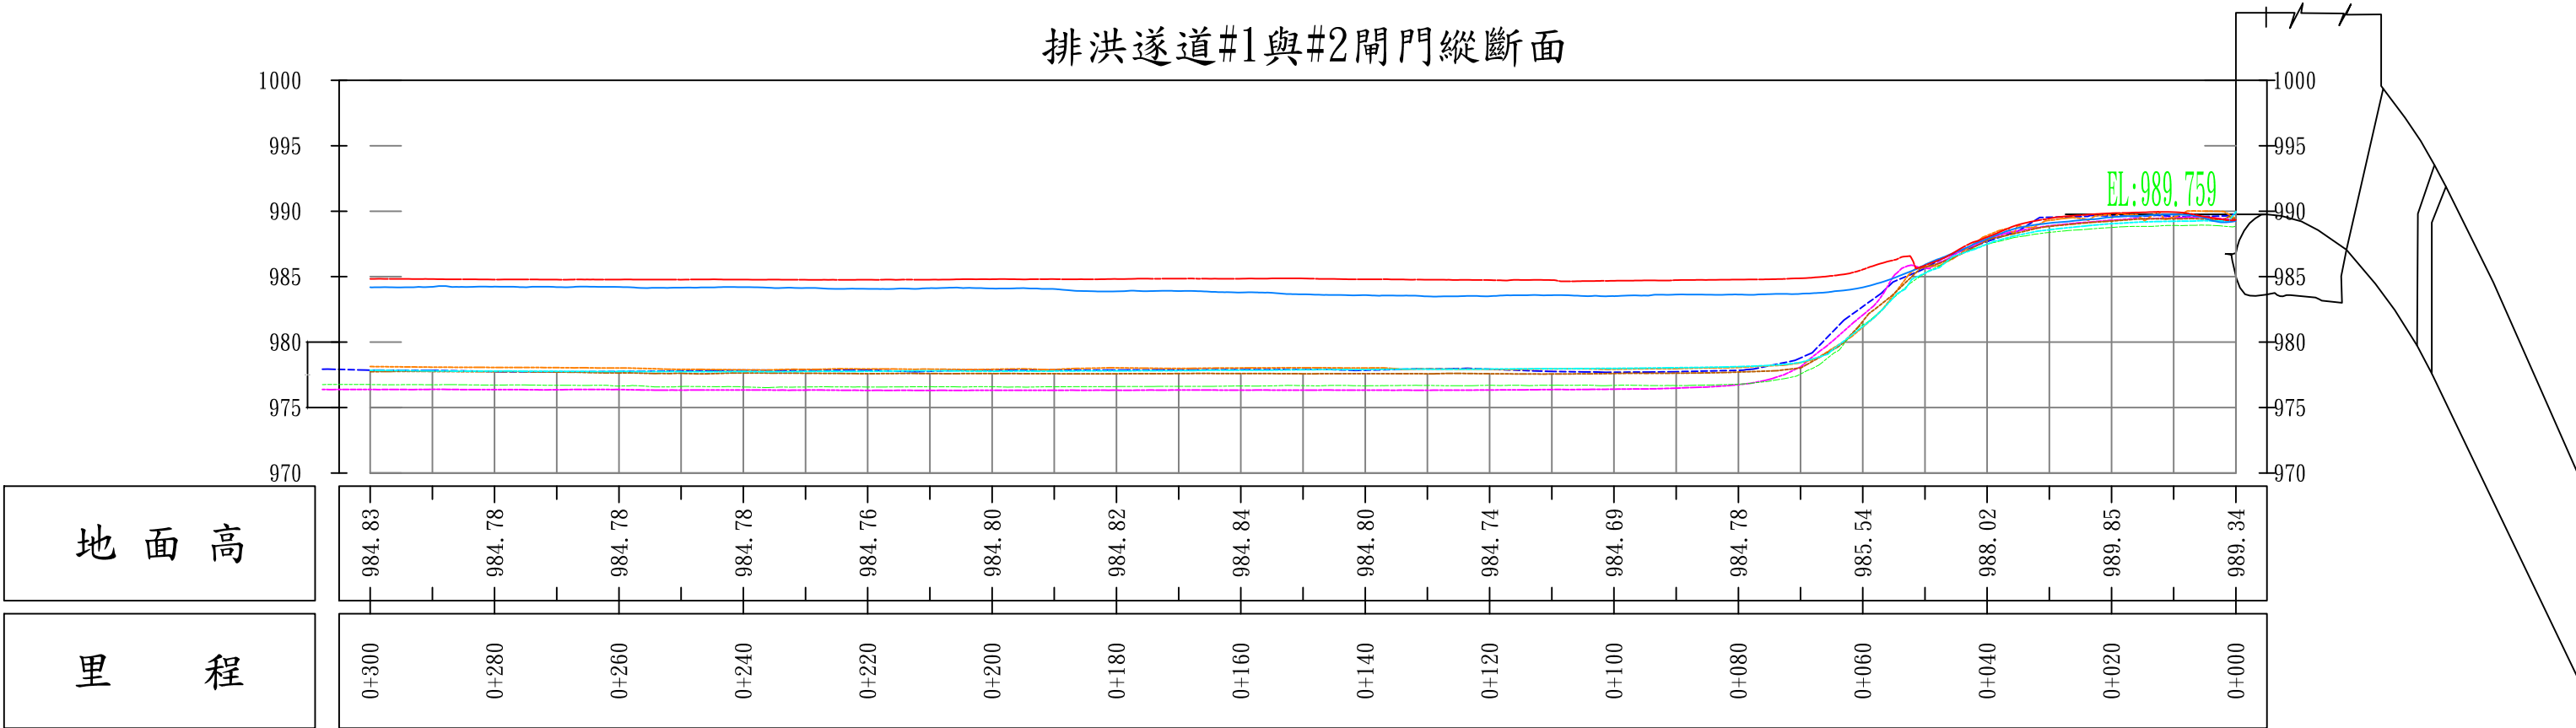

C' <---C

(3)排洪隧道#1與#2閘門前300公尺縱斷面圖

